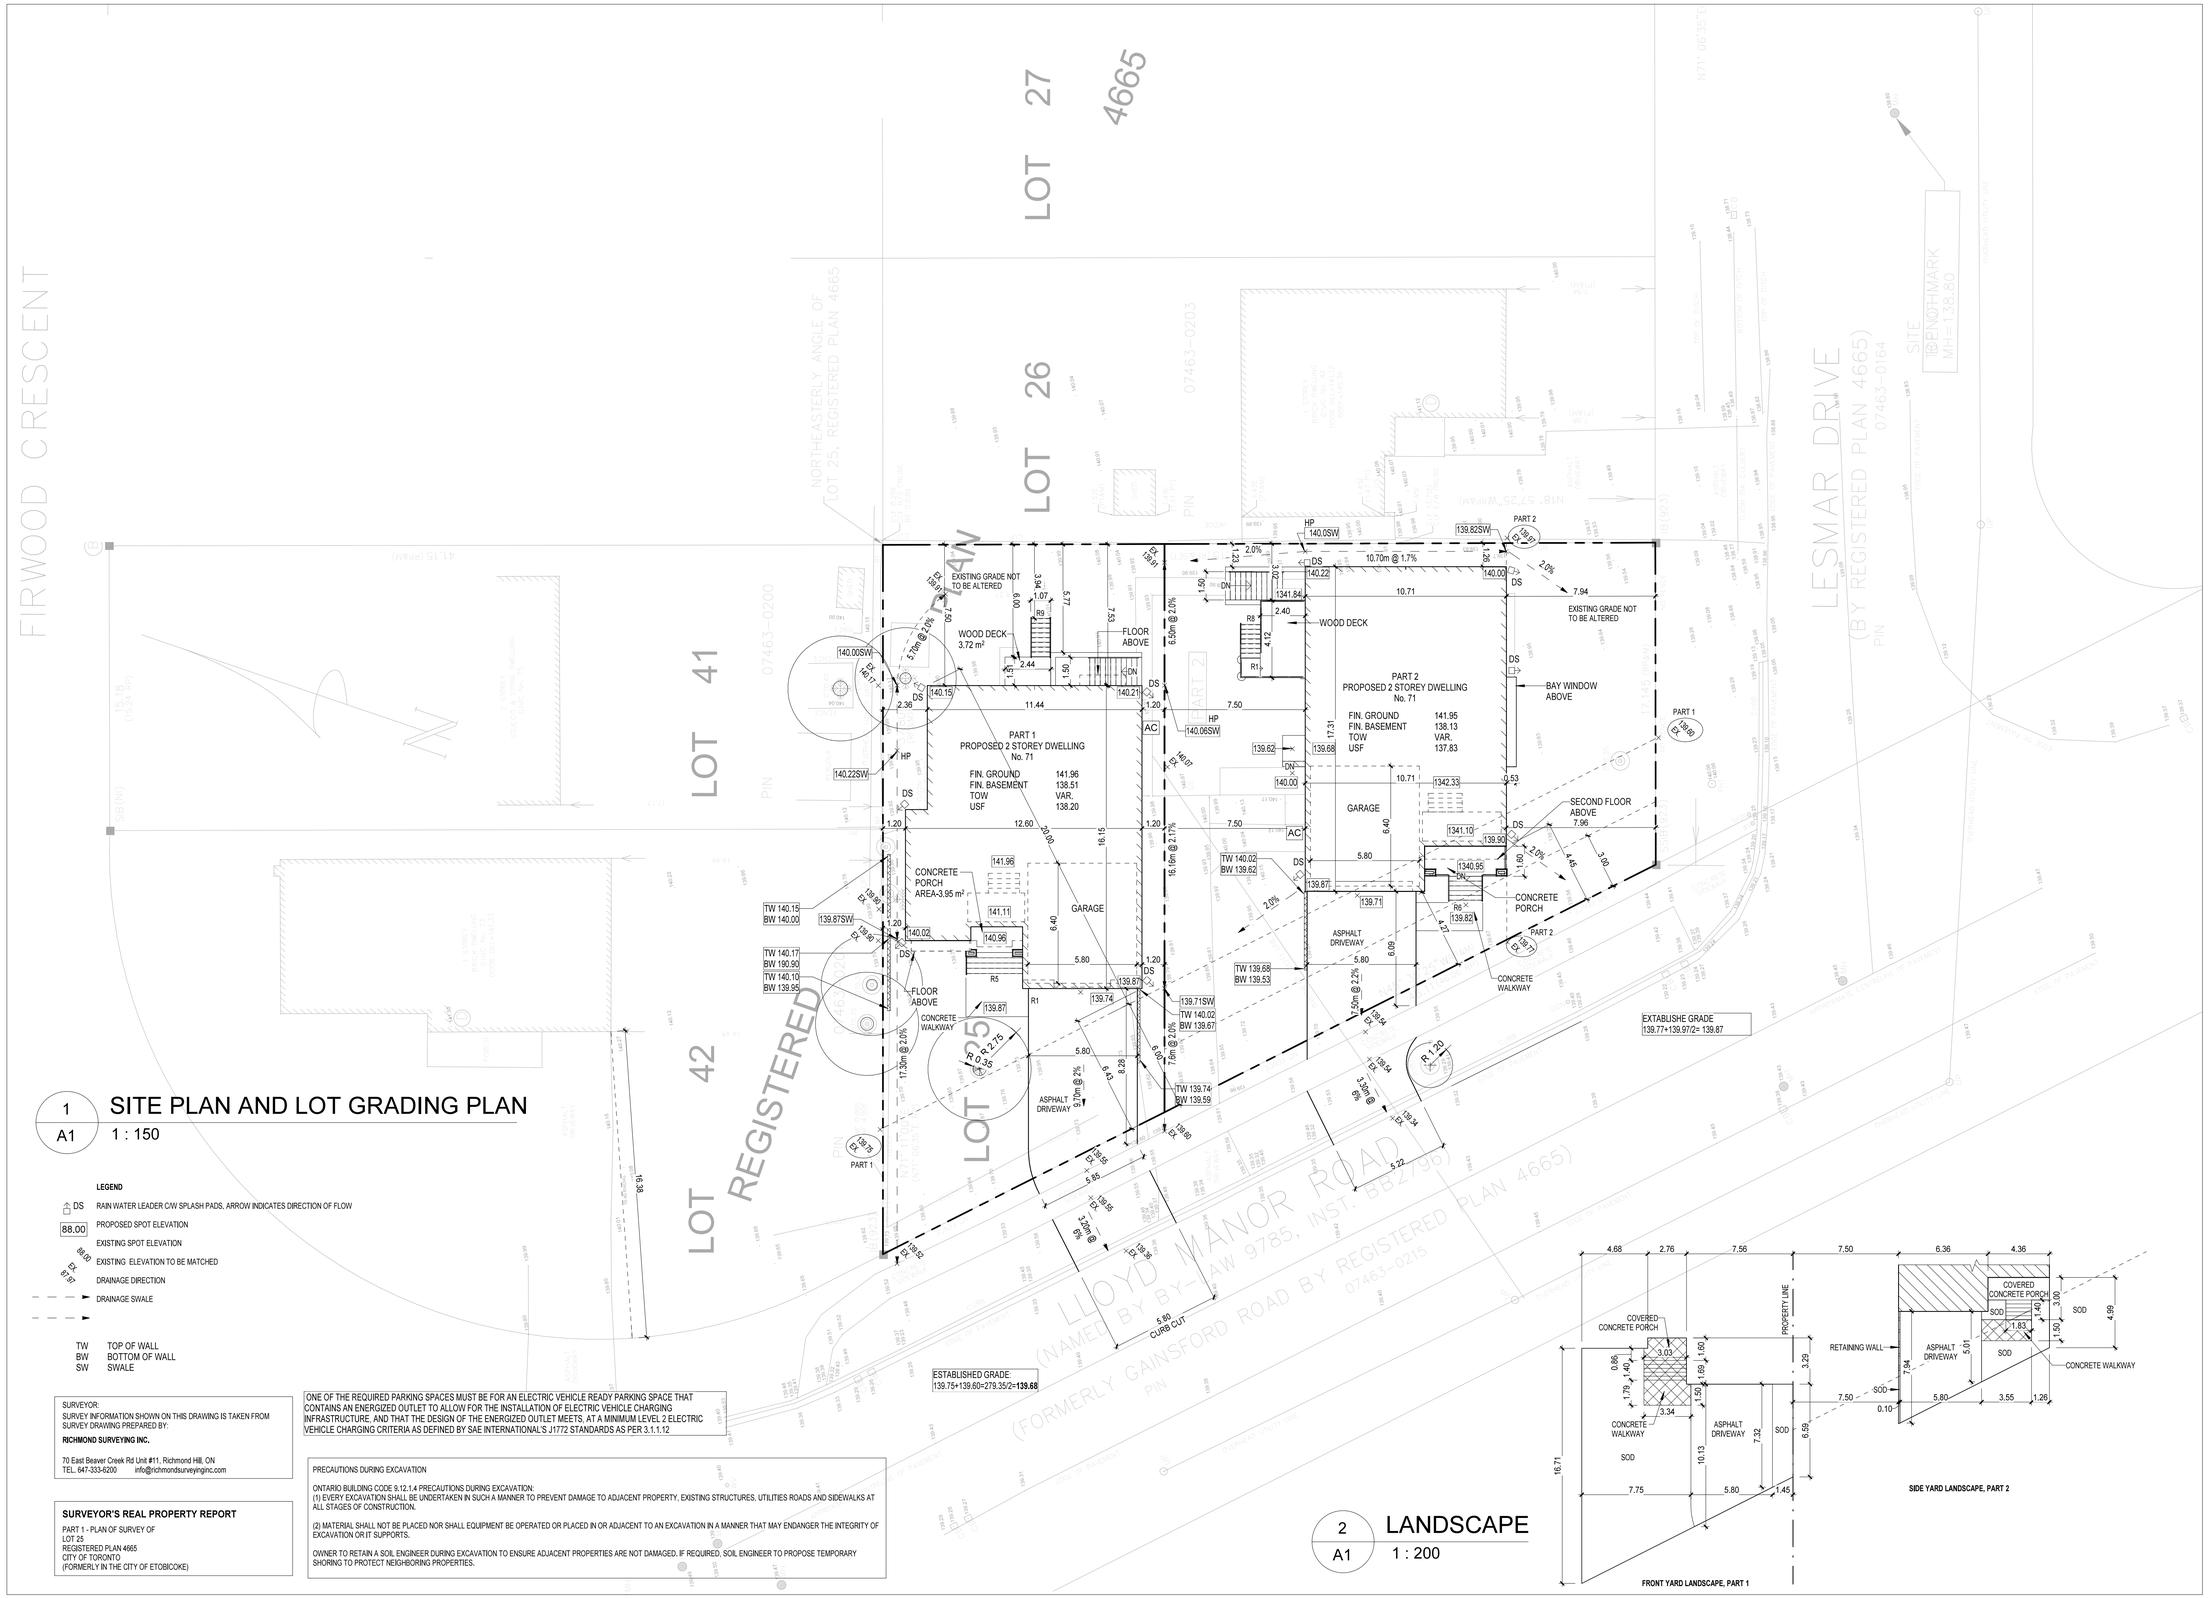

1 / A1 SITE PLAN AND LOT GRADING PLAN

1 : 150

LEGEND

DS	RAIN WATER LEADER C/W SPLASH PADS, ARROW INDICATES DIRECTION OF FLOW
88.00	PROPOSED SPOT ELEVATION
	EXISTING SPOT ELEVATION
89.00 EX	EXISTING ELEVATION TO BE MATCHED
85.97 EX	DRAINAGE DIRECTION
	DRAINAGE SWALE
TW	TOP OF WALL
BW	BOTTOM OF WALL
SW	SWALE

SURVEYOR:
SURVEY INFORMATION SHOWN ON THIS DRAWING IS TAKEN FROM SURVEY DRAWING PREPARED BY:

RICHMOND SURVEYING INC.

70 East Beaver Creek Rd Unit #11, Richmond Hill, ON
TEL. 647-333-6200 info@richmondsurveyinginc.com

SURVEYOR'S REAL PROPERTY REPORT

PART 1 - PLAN OF SURVEY OF
LOT 25
REGISTERED PLAN 4665
CITY OF TORONTO
(FORMERLY IN THE CITY OF ETOBICOKE)

ONE OF THE REQUIRED PARKING SPACES MUST BE FOR AN ELECTRIC VEHICLE READY PARKING SPACE THAT CONTAINS AN ENERGIZED OUTLET TO ALLOW FOR THE INSTALLATION OF ELECTRIC VEHICLE CHARGING INFRASTRUCTURE, AND THAT THE DESIGN OF THE ENERGIZED OUTLET MEETS, AT A MINIMUM LEVEL 2 ELECTRIC VEHICLE CHARGING CRITERIA AS DEFINED BY SAE INTERNATIONAL'S J1772 STANDARDS AS PER 3.1.1.12

PRECAUTIONS DURING EXCAVATION

ONTARIO BUILDING CODE 9.12.1.4 PRECAUTIONS DURING EXCAVATION:
(1) EVERY EXCAVATION SHALL BE UNDERTAKEN IN SUCH A MANNER TO PREVENT DAMAGE TO ADJACENT PROPERTY, EXISTING STRUCTURES, UTILITIES ROADS AND SIDEWALKS AT ALL STAGES OF CONSTRUCTION.

(2) MATERIAL SHALL NOT BE PLACED NOR SHALL EQUIPMENT BE OPERATED OR PLACED IN OR ADJACENT TO AN EXCAVATION IN A MANNER THAT MAY ENDANGER THE INTEGRITY OF EXCAVATION OR IT SUPPORTS.

OWNER TO RETAIN A SOIL ENGINEER DURING EXCAVATION TO ENSURE ADJACENT PROPERTIES ARE NOT DAMAGED, IF REQUIRED, SOIL ENGINEER TO PROPOSE TEMPORARY SHORING TO PROTECT NEIGHBORING PROPERTIES.

2 / A1 LANDSCAPE

1 : 200

NO.	REVISIONS	DATE
1	CITY COMMENTS	
CITY	ZONING APPLICATION	- - -

TO	ISSUED	DATE
	FOR STRUCTURAL ONLY	

GENERAL NOTES

ALL DRAWINGS ARE THE PROPERTY OF THE ARCHITECT AND THEY ARE NOT TO BE REPRODUCED IN WHOLE OR IN PART WITHOUT WRITTEN CONSENT FROM THE ARCHITECT.

CONTRACTOR TO CHECK AND VERIFY ALL DIMENSIONS BEFORE COMMENCING WORK AND TO REPORT ANY DISCREPANCIES TO THE ARCHITECT.

DO NOT SCALE DRAWINGS.

ALL CONSTRUCTION TO BE ACCORDING TO BEST COMMON PRACTICE AND CONFORM TO THE ONTARIO BUILDING CODE.

FOR ARCHITECTURAL ONLY

THIS DRAWING SHALL NOT BE USED FOR CONSTRUCTION PURPOSES UNTIL SIGNED BY THE ARCHITECT.

NIA Architects Inc.
10 MILNER BUSINESS COURT, SUITE 710
TORONTO, ONTARIO M1B 3C6
www: niarch.com E: info@niarch.com
T: 416-270-7810 F: 416-800-5434

PROJECT

PROPOSED DETACHED DUPLEX DWELLING

PART 1 AND PART 2

71 LLOYD MANOR ROAD, TORONTO

DRAWING

SITE PLAN AND LOT GRADING PLAN

DESIGNED A. SH.	PROJECT NO 2024-16
PROJECT STARTED SEP. 2024	FILE NAME
PLOTTED DATE FEB 25, 2026	DRAWING NO
SCALE As indicated	A1
CHECKED N.I.	