PROJECT STATISTICS, PART 1

SITE LOCATION	71 LLOYD MANOR ROAD, ETOBICOKE, ONTARIO		
ZONING	RD (f13.5; a510; d0.45)		
LOT AREA	REQUIRED SQM	PROVIDED SQM	SQF
	510	510.69	5,497.02

FORNTAGE

REQUIRED	PROVIDED
13.5 m	16.80 m

COVERAGE	LOT AREA	510.69
	SQM	%
PERMITTED	232.11	**45%**
PROPOSED	183.52	**36%**

HEIGHT	PERMITTED	PROPOSED
	10.0 m	10.71 m

SETBACKS	PERMITTED (m)	PROPOSED (m)
WEST (FRONT)	16.38	6.43
SOUTH (SIDE RIGHT)	1.2	1.2
EAST (REAR)	7.5	7.5
NORTH (LEFT SIDE)	1.2	1.2

DWELLING UNIT DEPTH	PERMITTED	PROPOSED
	19.0 m	20.0 m

DWELLING UNIT LENGTH	PERMITTED	PROPOSED
	17.0 m	16.15

FLOOR AREAS	SQM	SQF
PROPOSED:		
GROUND FLOOR AREA	178.99	1,926.63
SECOND FLOOR AREA	181.72	1,956.02
TOTAL FLOOR AREA	360.71	3,882.65

BASEMENT AREA	134.11	1,443.55
PROPOSED GARAGE AREA	43.76	471.03

FSI

10.20.40.40 (1)(C)
(C)the permitted maximum floor space index
does not apply to a duplex, triplex or fourplex. [By-law: 66-2024 Enacted]

PROJECT STATISTICS, PART 2

SITE LOCATION	71 LLOYD MANOR ROAD, ETOBICOKE, ONTARIO		
ZONING	RD (f13.5; a510; d0.45)		
LOT AREA	REQUIRED SQM	PROVIDED SQM	SQF
	510	620.50	6,679.00

FORNTAGE

REQUIRED	PROVIDED
13.5 m	17.14 m

COVERAGE	LOT AREA	620.50
	SQM	%
PERMITTED	282.02	**45%**
PROPOSED	183.75	**30%**

HEIGHT	PERMITTED	PROPOSED
	10.0 m	10.0 m

SETBACKS	PERMITTED (m)	PROPOSED (m)
SOUTH (FRONT)	7.94	7.94
EAST (SIDE RIGHT)	1.2	1.23
NORTH (REAR)	7.5	7.5
WEST (LEFT SIDE)	3	4.27

DWELLING UNIT DEPTH	PERMITTED	PROPOSED
	19.0 m	10.71

DWELLING UNIT LENGTH	PERMITTED	PROPOSED
	17.0 m	10.71

FLOOR AREAS	SQM	SQF
PROPOSED:		
GROUND FLOOR AREA	176.77	1,902.73
SECOND FLOOR AREA	175.86	1,892.94
TOTAL FLOOR AREA	352.63	3,795.67

BASEMENT AREA	130.05	1,399.85
PROPOSED GARAGE AREA	44.23	476.09

FSI

10.20.40.40 (1)(C)
(C)the permitted maximum floor space index
does not apply to a duplex, triplex or fourplex. [By-law: 66-2024 Enacted]

FRONT YARD LANDSCAPE, PART 1

	SQM	%	MATERIAL
FRONT YARD AREA	176.65	100.00	
DRIVEWAY AREA	52.72	29.84	ASPHALT
WALKWAY/PROCH/STEPS	14.62	8.28	CONCRETE
FRONT YARD LANDSCAPING	123.93	70.16	
SOFT LANDSCAPING	109.31	88.20	SOD

SIDE YARD LANDSCAPE, PART 2

	SQM	%	MATERIAL
SIDE YARD AREA	67.13	100.00%	
DRIVEWAY	37.56	55.96%	ASPHALT
LANDSCAPE AREA	29.56	44.04%	
WALKWAY/PROCH/STEPS/RETAINING WALL	15.27	51.66%	CONCRETE
SOFT LANDSCAPING	14.29	48.34%	SOD

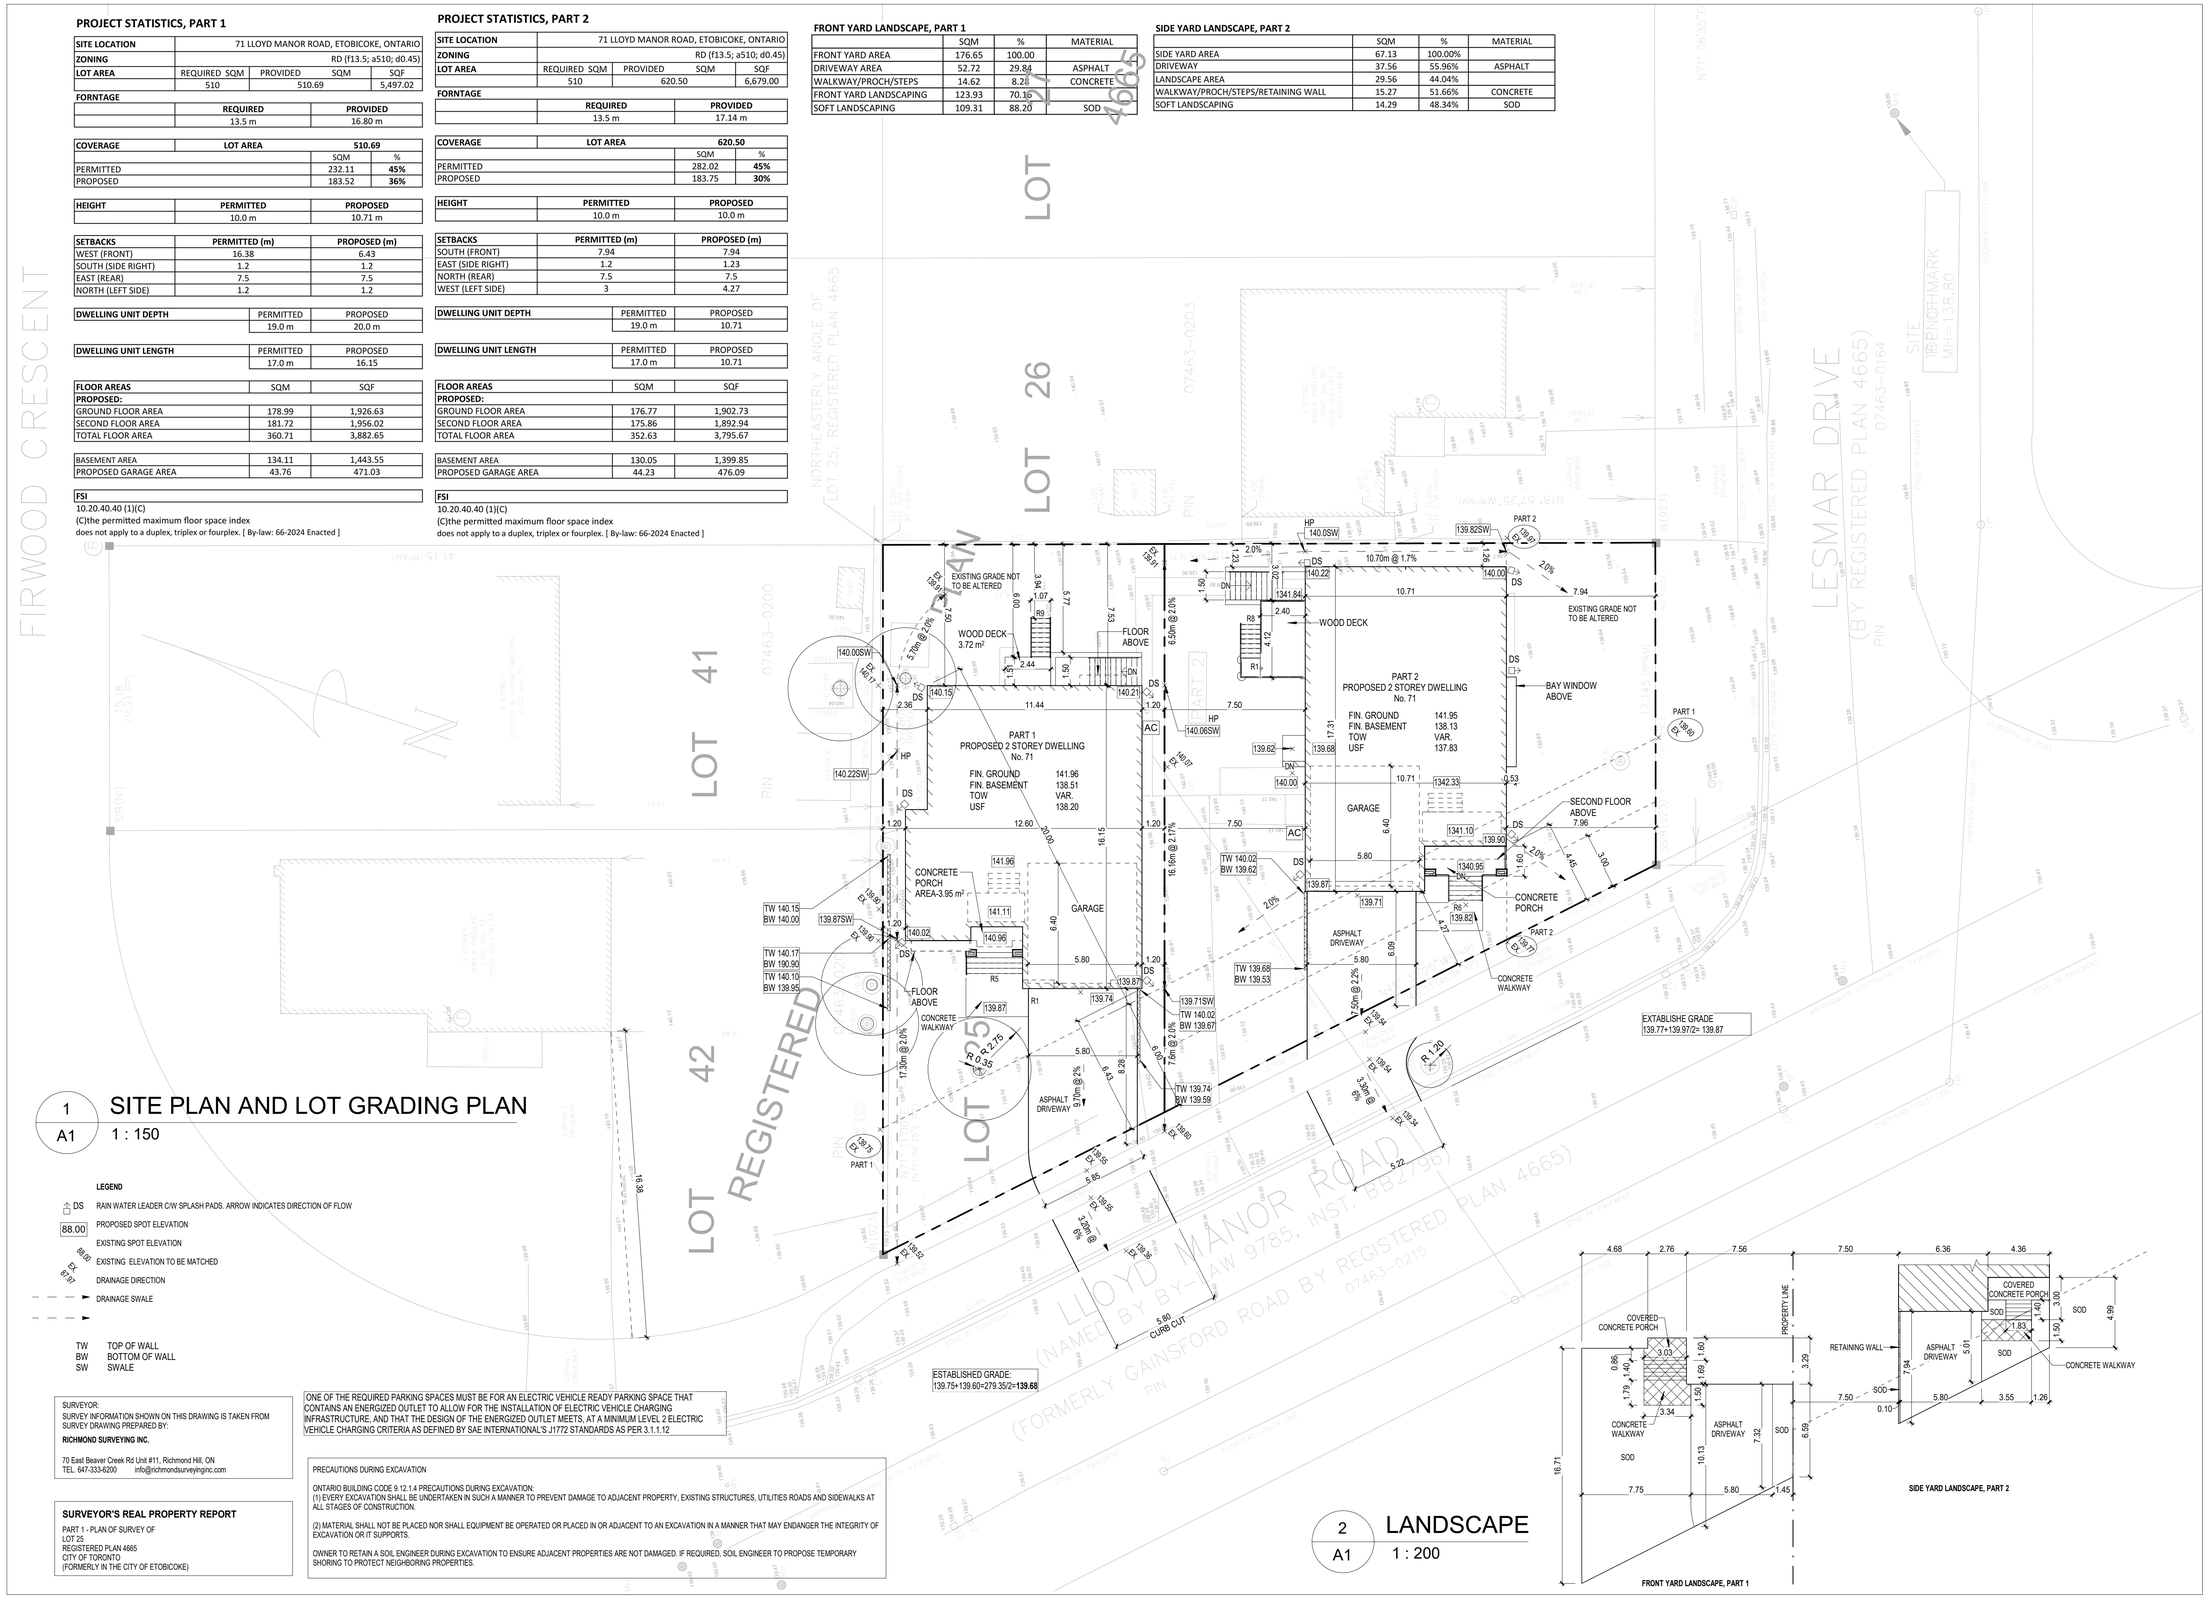

1 / A1 SITE PLAN AND LOT GRADING PLAN
1 : 150

LEGEND

DS	RAIN WATER LEADER C/W SPLASH PADS. ARROW INDICATES DIRECTION OF FLOW
88.00	PROPOSED SPOT ELEVATION
88.00	EXISTING SPOT ELEVATION
EX 89.00	EXISTING ELEVATION TO BE MATCHED
EX 85.07	DRAINAGE DIRECTION
	DRAINAGE SWALE
TW	TOP OF WALL
BW	BOTTOM OF WALL
SW	SWALE

SURVEYOR:
SURVEY INFORMATION SHOWN ON THIS DRAWING IS TAKEN FROM SURVEY DRAWING PREPARED BY:
RICHMOND SURVEYING INC.
70 East Beaver Creek Rd Unit #11, Richmond Hill, ON
TEL. 647-333-6200 info@richmondsurveyinginc.com

SURVEYOR'S REAL PROPERTY REPORT
PART 1 - PLAN OF SURVEY OF
LOT 25
REGISTERED PLAN 4665
CITY OF TORONTO
(FORMERLY IN THE CITY OF ETOBICOKE)

ONE OF THE REQUIRED PARKING SPACES MUST BE FOR AN ELECTRIC VEHICLE READY PARKING SPACE THAT CONTAINS AN ENERGIZED OUTLET TO ALLOW FOR THE INSTALLATION OF ELECTRIC VEHICLE CHARGING INFRASTRUCTURE, AND THAT THE DESIGN OF THE ENERGIZED OUTLET MEETS, AT A MINIMUM LEVEL 2 ELECTRIC VEHICLE CHARGING CRITERIA AS DEFINED BY SAE INTERNATIONAL'S J1772 STANDARDS AS PER 3.1.1.12

PRECAUTIONS DURING EXCAVATION

ONTARIO BUILDING CODE 9.12.1.4 PRECAUTIONS DURING EXCAVATION:
(1) EVERY EXCAVATION SHALL BE UNDERTAKEN IN SUCH A MANNER TO PREVENT DAMAGE TO ADJACENT PROPERTY, EXISTING STRUCTURES, UTILITIES ROADS AND SIDEWALKS AT ALL STAGES OF CONSTRUCTION.

(2) MATERIAL SHALL NOT BE PLACED NOR SHALL EQUIPMENT BE OPERATED OR PLACED IN OR ADJACENT TO AN EXCAVATION IN A MANNER THAT MAY ENDANGER THE INTEGRITY OF EXCAVATION OR IT SUPPORTS.

OWNER TO RETAIN A SOIL ENGINEER DURING EXCAVATION TO ENSURE ADJACENT PROPERTIES ARE NOT DAMAGED. IF REQUIRED, SOIL ENGINEER TO PROPOSE TEMPORARY SHORING TO PROTECT NEIGHBORING PROPERTIES.

2 / A1 LANDSCAPE
1 : 200

NO.	REVISIONS	DATE
1	CITY COMMENTS	

CITY	ZONING APPLICATION	- .-.-
TO	**ISSUED**	**DATE**

FOR STRUCTURAL ONLY

GENERAL NOTES

ALL DRAWINGS ARE THE PROPERTY OF THE ARCHITECT AND THEY ARE NOT TO BE REPRODUCED IN WHOLE OR IN PART WITHOUT WRITTEN CONSENT FROM THE ARCHITECT.

CONTRACTOR TO CHECK AND VERIFY ALL DIMENSIONS BEFORE COMMENCING WORK AND TO REPORT ANY DISCREPANCIES TO THE ARCHITECT.

DO NOT SCALE DRAWINGS.

ALL CONSTRUCTION TO BE ACCORDING TO BEST COMMON PRACTICE AND CONFORM TO THE ONTARIO BUILDING CODE.

FOR ARCHITECTURAL ONLY

THIS DRAWING SHALL NOT BE USED FOR CONSTRUCTION PURPOSES UNTIL SIGNED BY THE ARCHITECT.

NIA Architects Inc.
10 MILNER BUSINESS COURT, SUITE 710
TORONTO, ONTARIO M1B 3C6
www: niarch.com E: info@niarch.com
T: 416-270-7810 F: 416-800-5434

PROJECT
PROPOSED DETACHED DUPLEX DWELLING
PART 1 AND PART 2
71 LLOYD MANOR ROAD, TORONTO

DRAWING
SITE PLAN AND LOT GRADING PLAN

DESIGNED A. SH.	PROJECT NO 2024-16
PROJECT STARTED SEP. 2024	FILE NAME
PLOTTED DATE FEB 25, 2026	DRAWING NO
SCALE As indicated	A1
CHECKED N.I.	