## PROJECT STATISTICS, PART 1

| | | | |
|---|---|---|---|
| **SITE LOCATION** | 71 LLOYD MANOR ROAD, ETOBICOKE, ONTARIO | | |
| **ZONING** | RD (f13.5; a510; d0.45) | | |
| **LOT AREA** | REQUIRED SQM | PROVIDED SQM | SQF |
| | 510 | 510.69 | 5,497.02 |

**FORNTAGE**

| REQUIRED | PROVIDED |
|---|---|
| 13.5 m | 16.80 m |

| **COVERAGE** | **LOT AREA** | **510.69** |
|---|---|---|
| | SQM | % |
| PERMITTED | 232.11 | **45%** |
| PROPOSED | 183.52 | **36%** |

| **HEIGHT** | **PERMITTED** | **PROPOSED** |
|---|---|---|
| | 10.0 m | 10.71 m |

| **SETBACKS** | **PERMITTED (m)** | **PROPOSED (m)** |
|---|---|---|
| WEST (FRONT) | 16.38 | 6.43 |
| SOUTH (SIDE RIGHT) | 1.2 | 1.2 |
| EAST (REAR) | 7.5 | 7.5 |
| NORTH (LEFT SIDE) | 1.2 | 1.2 |

| **DWELLING UNIT DEPTH** | PERMITTED | PROPOSED |
|---|---|---|
| | 19.0 m | 20.0 m |

| **DWELLING UNIT LENGTH** | PERMITTED | PROPOSED |
|---|---|---|
| | 17.0 m | 16.15 |

| **FLOOR AREAS** | SQM | SQF |
|---|---|---|
| **PROPOSED:** | | |
| GROUND FLOOR AREA | 178.99 | 1,926.63 |
| SECOND FLOOR AREA | 181.72 | 1,956.02 |
| TOTAL FLOOR AREA | 360.71 | 3,882.65 |

| | | |
|---|---|---|
| BASEMENT AREA | 134.11 | 1,443.55 |
| PROPOSED GARAGE AREA | 43.76 | 471.03 |

**FSI**

10.20.40.40 (1)(C)
(C)the permitted maximum floor space index
does not apply to a duplex, triplex or fourplex. [ By-law: 66-2024 Enacted ]

## PROJECT STATISTICS, PART 2

| | | | |
|---|---|---|---|
| **SITE LOCATION** | 71 LLOYD MANOR ROAD, ETOBICOKE, ONTARIO | | |
| **ZONING** | RD (f13.5; a510; d0.45) | | |
| **LOT AREA** | REQUIRED SQM | PROVIDED SQM | SQF |
| | 510 | 620.50 | 6,679.00 |

**FORNTAGE**

| REQUIRED | PROVIDED |
|---|---|
| 13.5 m | 17.14 m |

| **COVERAGE** | **LOT AREA** | **620.50** |
|---|---|---|
| | SQM | % |
| PERMITTED | 282.02 | **45%** |
| PROPOSED | 183.75 | **30%** |

| **HEIGHT** | **PERMITTED** | **PROPOSED** |
|---|---|---|
| | 10.0 m | 10.0 m |

| **SETBACKS** | **PERMITTED (m)** | **PROPOSED (m)** |
|---|---|---|
| SOUTH (FRONT) | 7.94 | 7.94 |
| EAST (SIDE RIGHT) | 1.2 | 1.23 |
| NORTH (REAR) | 7.5 | 7.5 |
| WEST (LEFT SIDE) | 3 | 4.27 |

| **DWELLING UNIT DEPTH** | PERMITTED | PROPOSED |
|---|---|---|
| | 19.0 m | 10.71 |

| **DWELLING UNIT LENGTH** | PERMITTED | PROPOSED |
|---|---|---|
| | 17.0 m | 10.71 |

| **FLOOR AREAS** | SQM | SQF |
|---|---|---|
| **PROPOSED:** | | |
| GROUND FLOOR AREA | 176.77 | 1,902.73 |
| SECOND FLOOR AREA | 175.86 | 1,892.94 |
| TOTAL FLOOR AREA | 352.63 | 3,795.67 |

| | | |
|---|---|---|
| BASEMENT AREA | 130.05 | 1,399.85 |
| PROPOSED GARAGE AREA | 44.23 | 476.09 |

**FSI**

10.20.40.40 (1)(C)
(C)the permitted maximum floor space index
does not apply to a duplex, triplex or fourplex. [ By-law: 66-2024 Enacted ]

**FRONT YARD LANDSCAPE, PART 1**

| | SQM | % | MATERIAL |
|---|---|---|---|
| FRONT YARD AREA | 176.65 | 100.00 | |
| DRIVEWAY AREA | 52.72 | 29.84 | ASPHALT |
| WALKWAY/PROCH/STEPS | 14.62 | 8.28 | CONCRETE |
| FRONT YARD LANDSCAPING | 123.93 | 70.16 | |
| SOFT LANDSCAPING | 109.31 | 88.20 | SOD |

**SIDE YARD LANDSCAPE, PART 2**

| | SQM | % | MATERIAL |
|---|---|---|---|
| SIDE YARD AREA | 67.13 | 100.00% | |
| DRIVEWAY | 37.56 | 55.96% | ASPHALT |
| LANDSCAPE AREA | 29.56 | 44.04% | |
| WALKWAY/PROCH/STEPS/RETAINING WALL | 15.27 | 51.66% | CONCRETE |
| SOFT LANDSCAPING | 14.29 | 48.34% | SOD |

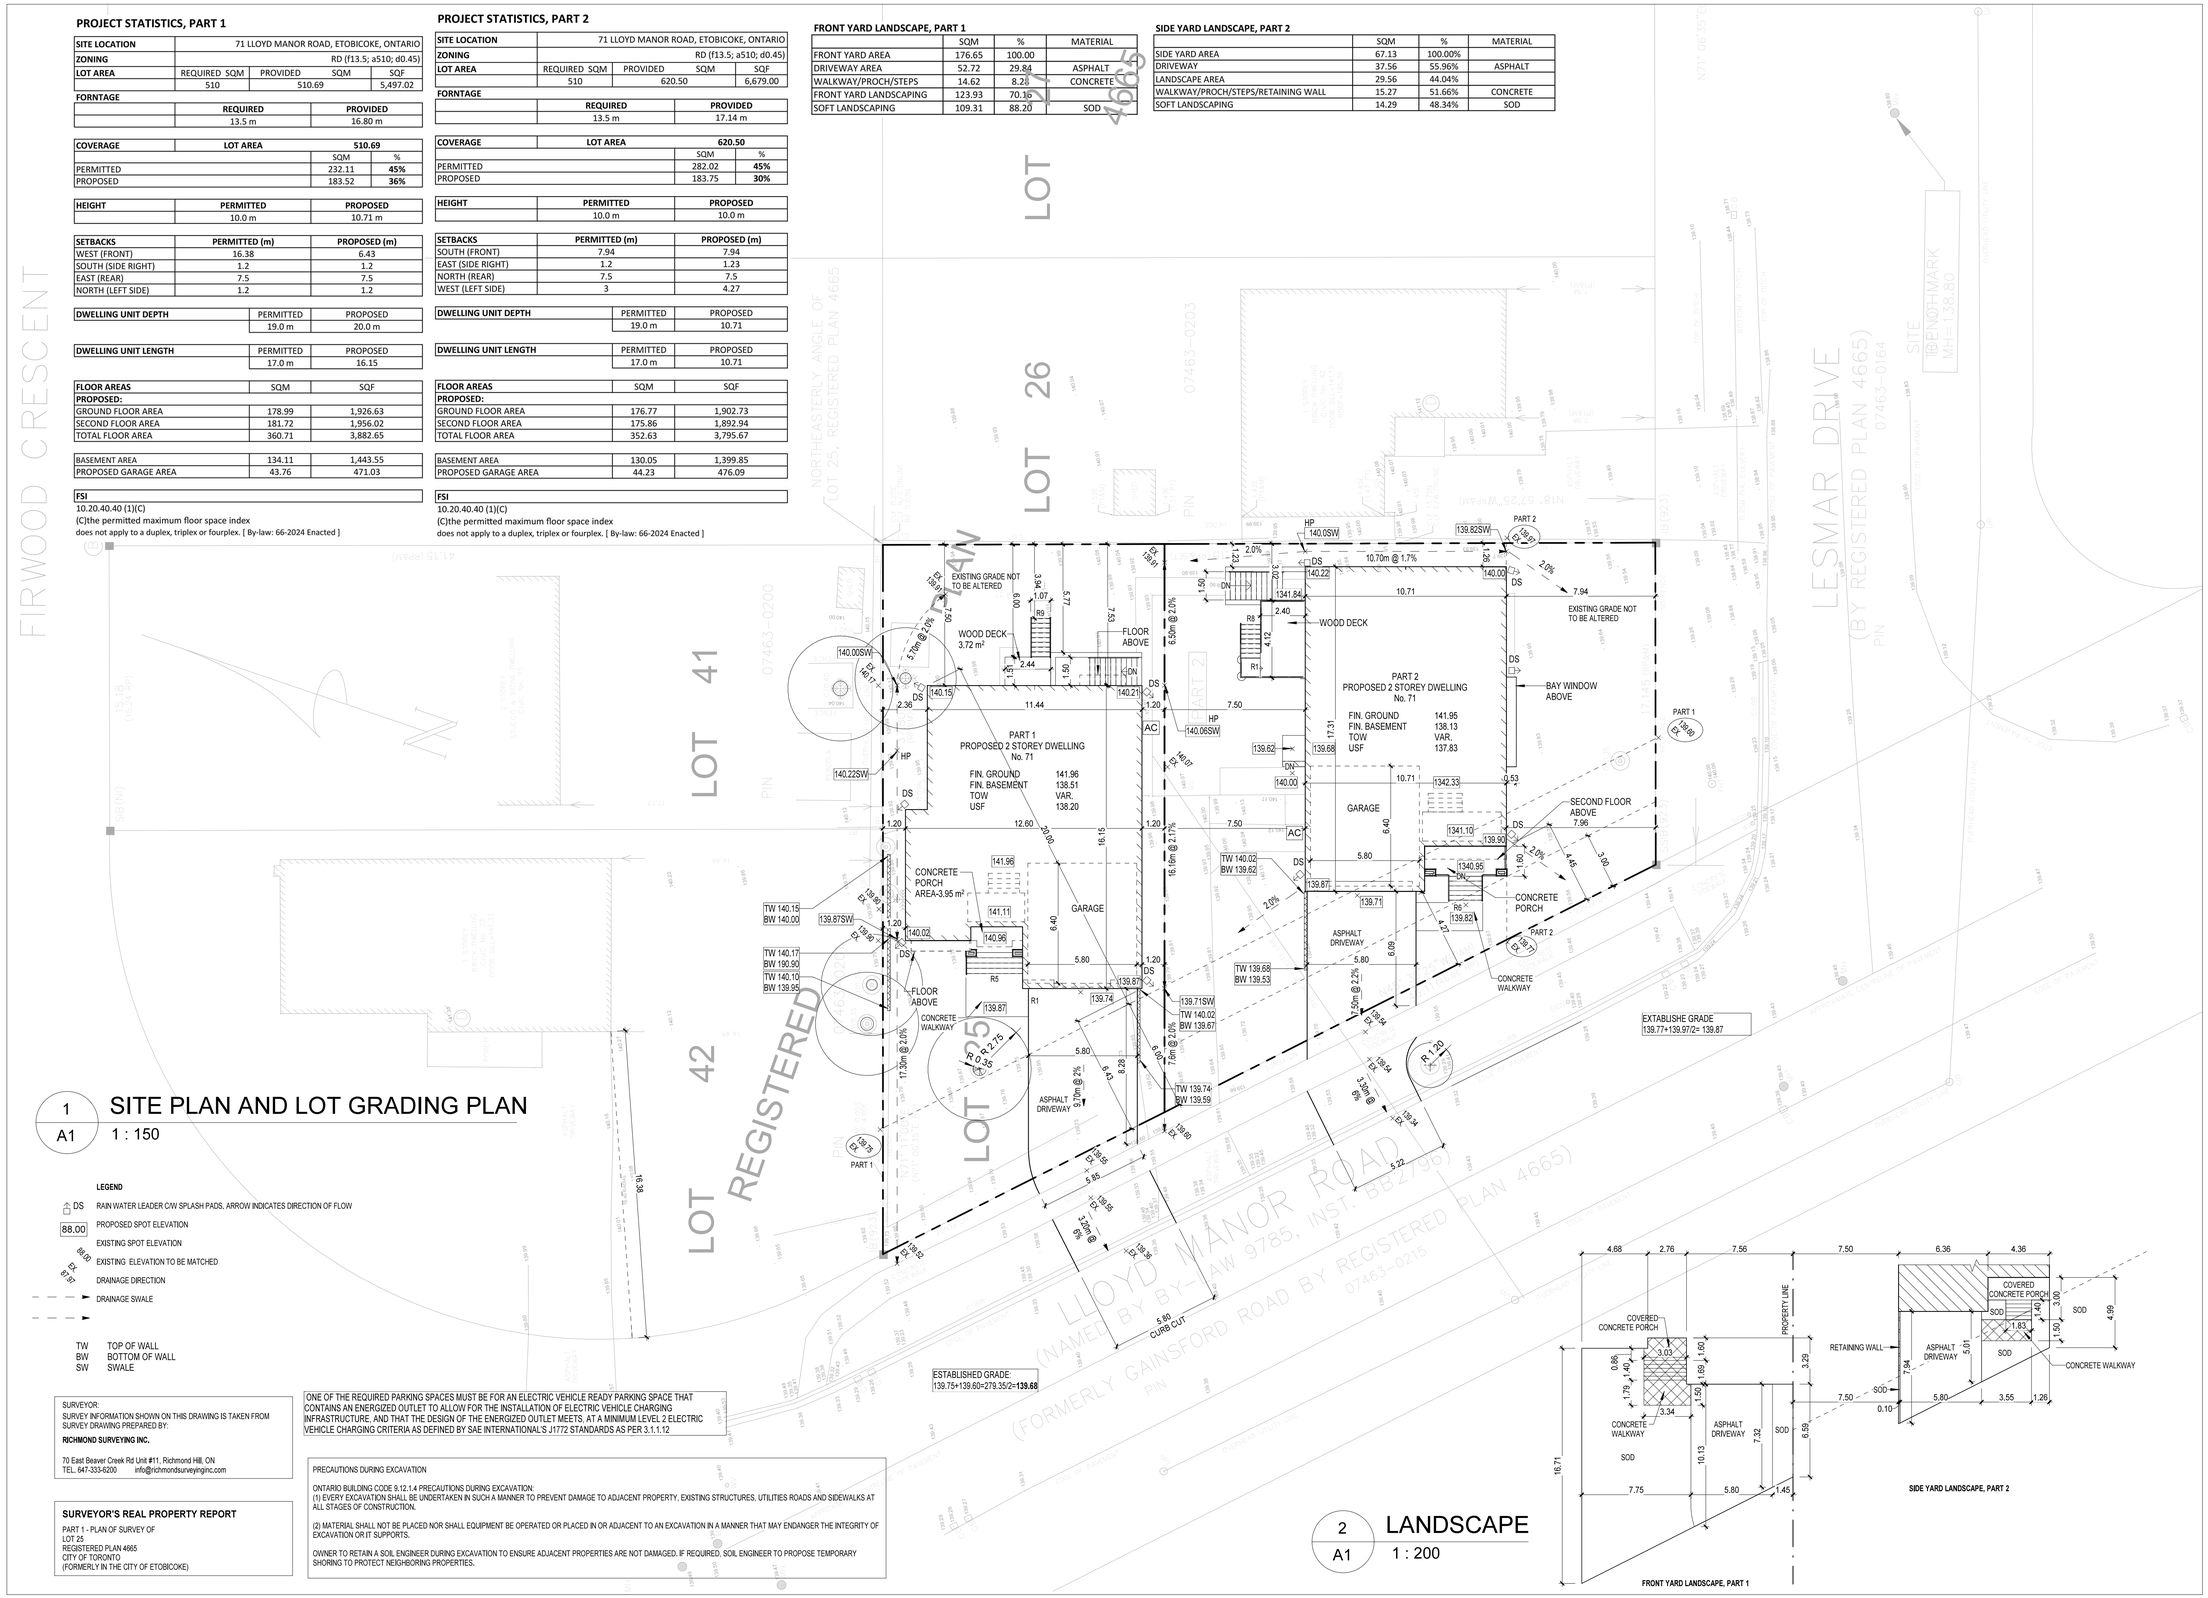


1 / A1 SITE PLAN AND LOT GRADING PLAN
1 : 150

**LEGEND**

| | |
|---|---|
| DS | RAIN WATER LEADER C/W SPLASH PADS, ARROW INDICATES DIRECTION OF FLOW |
| 88.00 | PROPOSED SPOT ELEVATION |
| | EXISTING SPOT ELEVATION |
| 89.00 EX | EXISTING ELEVATION TO BE MATCHED |
| EX 85.97 | DRAINAGE DIRECTION |
| | DRAINAGE SWALE |
| | |
| TW | TOP OF WALL |
| BW | BOTTOM OF WALL |
| SW | SWALE |

SURVEYOR:
SURVEY INFORMATION SHOWN ON THIS DRAWING IS TAKEN FROM SURVEY DRAWING PREPARED BY:
**RICHMOND SURVEYING INC.**
70 East Beaver Creek Rd Unit #11, Richmond Hill, ON
TEL. 647-333-6200 info@richmondsurveyinginc.com

**SURVEYOR'S REAL PROPERTY REPORT**
PART 1 - PLAN OF SURVEY OF
LOT 25
REGISTERED PLAN 4665
CITY OF TORONTO
(FORMERLY IN THE CITY OF ETOBICOKE)

ONE OF THE REQUIRED PARKING SPACES MUST BE FOR AN ELECTRIC VEHICLE READY PARKING SPACE THAT CONTAINS AN ENERGIZED OUTLET TO ALLOW FOR THE INSTALLATION OF ELECTRIC VEHICLE CHARGING INFRASTRUCTURE, AND THAT THE DESIGN OF THE ENERGIZED OUTLET MEETS, AT A MINIMUM LEVEL 2 ELECTRIC VEHICLE CHARGING CRITERIA AS DEFINED BY SAE INTERNATIONAL'S J1772 STANDARDS AS PER 3.1.1.12

PRECAUTIONS DURING EXCAVATION

ONTARIO BUILDING CODE 9.12.1.4 PRECAUTIONS DURING EXCAVATION:
(1) EVERY EXCAVATION SHALL BE UNDERTAKEN IN SUCH A MANNER TO PREVENT DAMAGE TO ADJACENT PROPERTY, EXISTING STRUCTURES, UTILITIES ROADS AND SIDEWALKS AT ALL STAGES OF CONSTRUCTION.

(2) MATERIAL SHALL NOT BE PLACED NOR SHALL EQUIPMENT BE OPERATED OR PLACED IN OR ADJACENT TO AN EXCAVATION IN A MANNER THAT MAY ENDANGER THE INTEGRITY OF EXCAVATION OR IT SUPPORTS.

OWNER TO RETAIN A SOIL ENGINEER DURING EXCAVATION TO ENSURE ADJACENT PROPERTIES ARE NOT DAMAGED, IF REQUIRED, SOIL ENGINEER TO PROPOSE TEMPORARY SHORING TO PROTECT NEIGHBORING PROPERTIES.

2 / A1 LANDSCAPE
1 : 200




| NO. | REVISIONS | DATE |
|---|---|---|
| 1 | CITY COMMENTS | |

| TO | ISSUED | DATE |
|---|---|---|
| CITY | ZONING APPLICATION | - - - |

FOR STRUCTURAL ONLY

**GENERAL NOTES**

ALL DRAWINGS ARE THE PROPERTY OF THE ARCHITECT AND THEY ARE NOT TO BE REPRODUCED IN WHOLE OR IN PART WITHOUT WRITTEN CONSENT FROM THE ARCHITECT.

CONTRACTOR TO CHECK AND VERIFY ALL DIMENSIONS BEFORE COMMENCING WORK AND TO REPORT ANY DISCREPANCIES TO THE ARCHITECT.

DO NOT SCALE DRAWINGS.

ALL CONSTRUCTION TO BE ACCORDING TO BEST COMMON PRACTICE AND CONFORM TO THE ONTARIO BUILDING CODE.

FOR ARCHITECTURAL ONLY

THIS DRAWING SHALL NOT BE USED FOR CONSTRUCTION PURPOSES UNTIL SIGNED BY THE ARCHITECT.


NIA Architects Inc.
10 MILNER BUSINESS COURT, SUITE 710
TORONTO, ONTARIO M1B 3C6
www: niarch.com E: info@niarch.com
T: 416-270-7810 F: 416-800-5434


PROJECT
PROPOSED DETACHED DUPLEX DWELLING
PART 1 AND PART 2
71 LLOYD MANOR ROAD, TORONTO

DRAWING
SITE PLAN AND LOT GRADING PLAN

| | |
|---|---|
| DESIGNED A. SH. | PROJECT NO 2024-16 |
| PROJECT STARTED SEP. 2024 | FILE NAME |
| PLOTTED DATE FEB 25, 2026 | DRAWING NO |
| SCALE As indicated | A1 |
| CHECKED N.I. | |