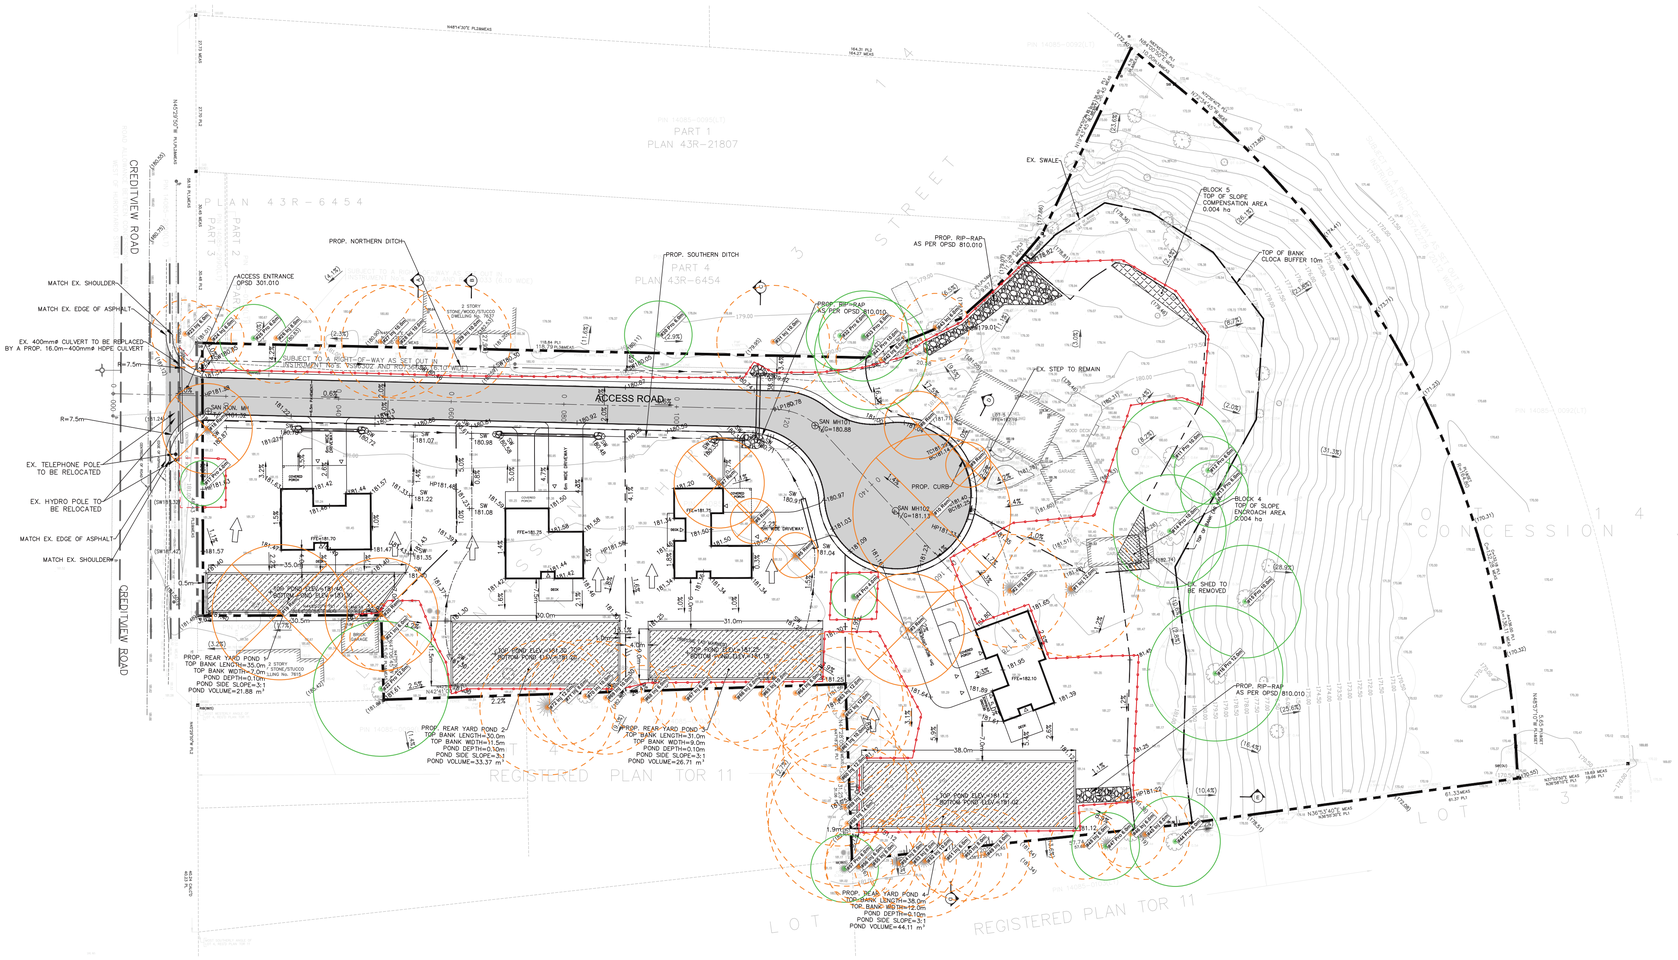

TREE PROTECTION SPECIFICATION

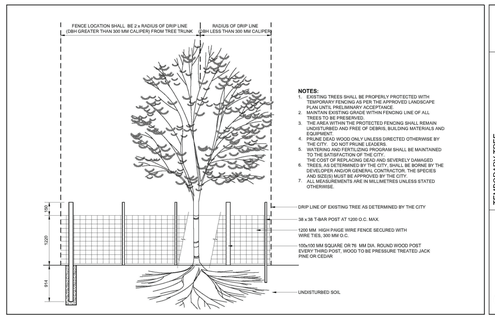

TREE INVENTORY

TREE DOCTORS
PROFESSIONAL TREE CARE

Tree Doctors Inc.
343 Olivewood Road, Toronto ON, M8Z 2Z6
info@treedoctors.ca | (416) 201-8000

PROJECT TITLE (PROPERTY ADDRESS):
7631 Creditview Road, Brampton

CLIENT: Owner(s)

KEY PLAN:

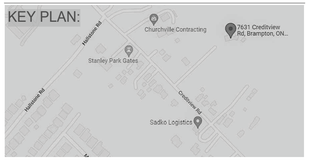

LEGEND

- TREES TO REMAIN / TREE PROTECTION ZONE (TPZ)
- TREES TO BE REMOVED
- TREES TO BE INJURED
- SNOW FENCE HOARDING
- PLYWOOD FENCE HOARDING PHASE 1
- PLYWOOD FENCE HOARDING PHASE 2
- HORIZONTAL TREE PROTECTION
- ROOTS SENSITIVE EXCAVATION (R.S.E.)
- TREE REPLANTING LOCATION
- PRIMARY ACCESS ROUTE

Detailed Tree Inventory Table

- Tree to be removed/injured
- Tree to be preserved

Tree Protection Plan

TP1

Notes:
TO BE READ IN CONJUNCTION WITH CORRESPONDING ARBORIST REPORT

All rights reserved by the Arborist. These Drawings & Specs are confidential and shall remain the sole property of the company. They shall not be reproduced (in whole or in part), shared with third parties or used in any manner on other projects or extensions to this project without the prior written consent of the company.

SCALE: 1:500

Serg Litvinov
Certified Arborist
ISA #ON-2281A

CURRENT	SL	03.11.26
INITIAL	SL	01/01/26
REVISION	NAME	DATE

ALL PREVIOUS ISSUES OF THIS DRAWING ARE SUPERSEDED