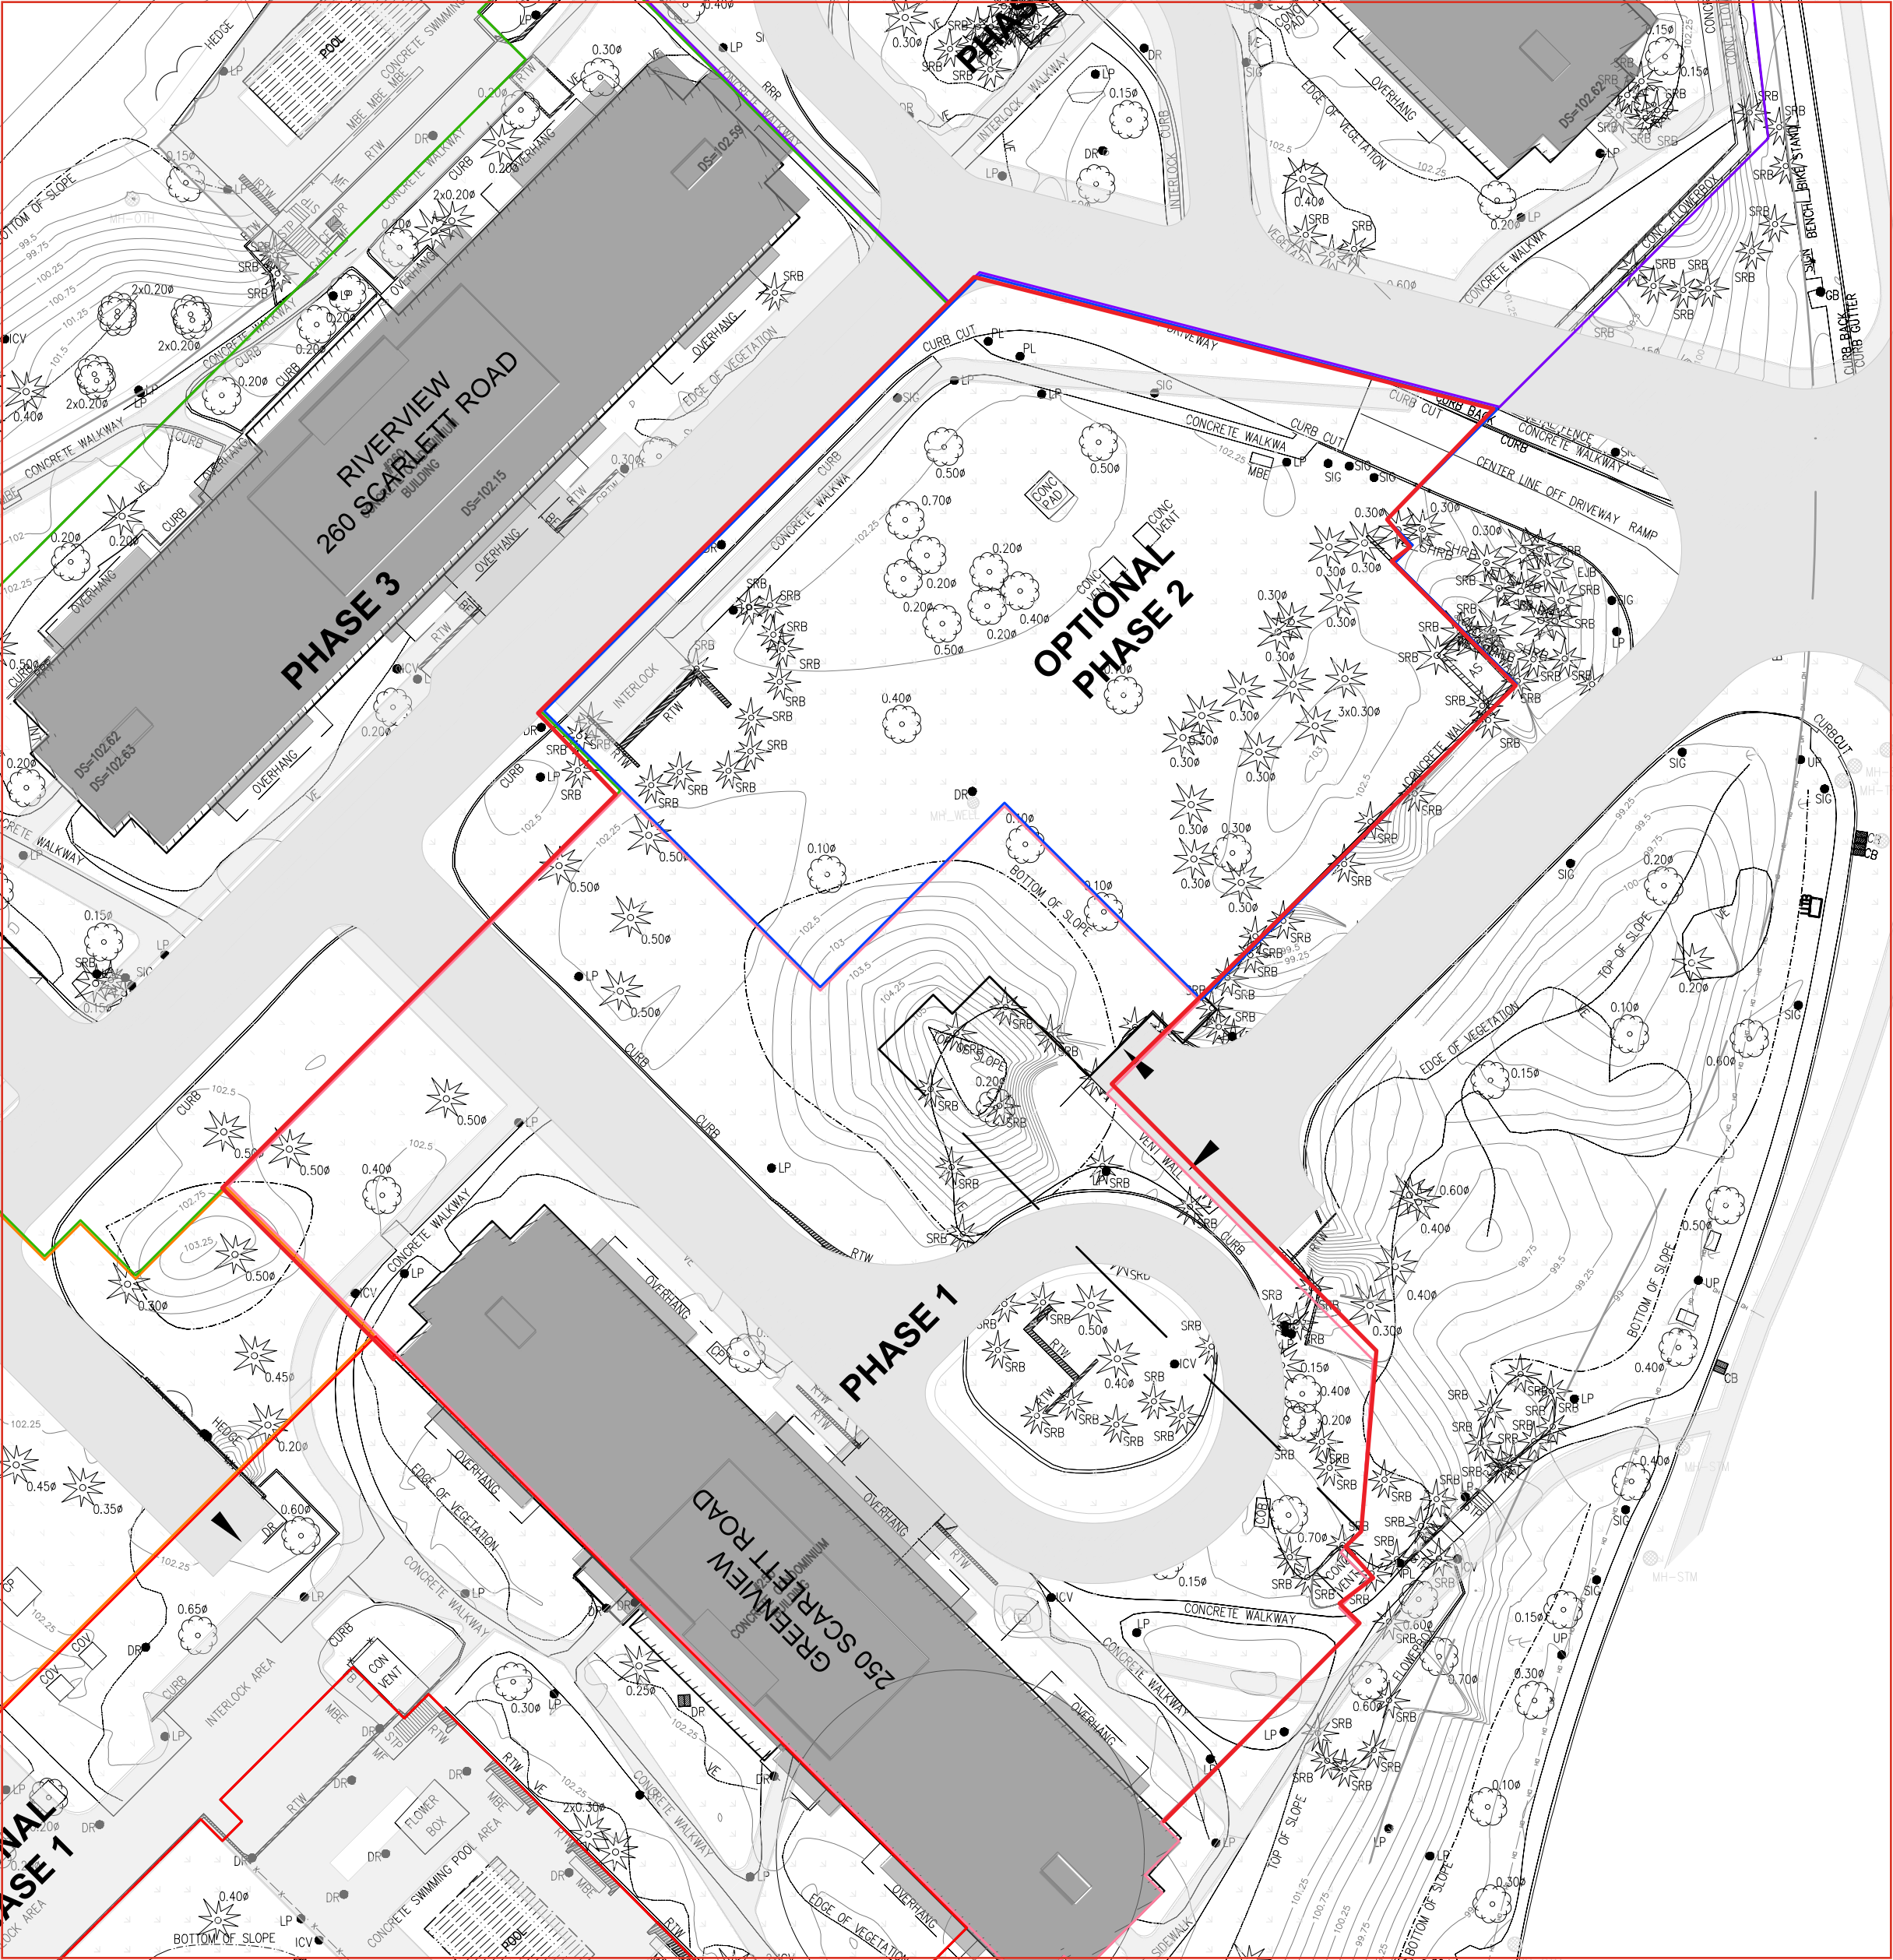
RIVERVIEW
260 SCARLETT ROAD
PHASE 3
OPTIONAL PHASE 2
PHASE 1
GREENVIEW
250 SCARLETT ROAD
CONCRETE WALKWAY
OVERHANG
EDGE OF VEGETATION
CURB
INTERLOCK
CONCRETE SWIMMING POOL AREA
POOL
FLOWER BOX
INTERLOCK AREA
BOTTOM OF SLOPE
TOP OF SLOPE
CONC PAD
CONC VENT
VENT WALL
CONCRETE WALL
CENTER LINE OFF DRIVEWAY RAMP
CURB CUT
CURB BACK
CURB GUTTER
CONC FLOWERBOX
BIKE STAND
BENCH
SIGN
DS=102.62
DS=102.59
DS=102.15
DS=102.63
DS=102.62